

-note-

갑
소
배 배연창
완 완강기
사 사다리


1 / A

(오피스텔)
지상2층 평면도

축 척 : 1/150

DRAWING NO.

A- 55

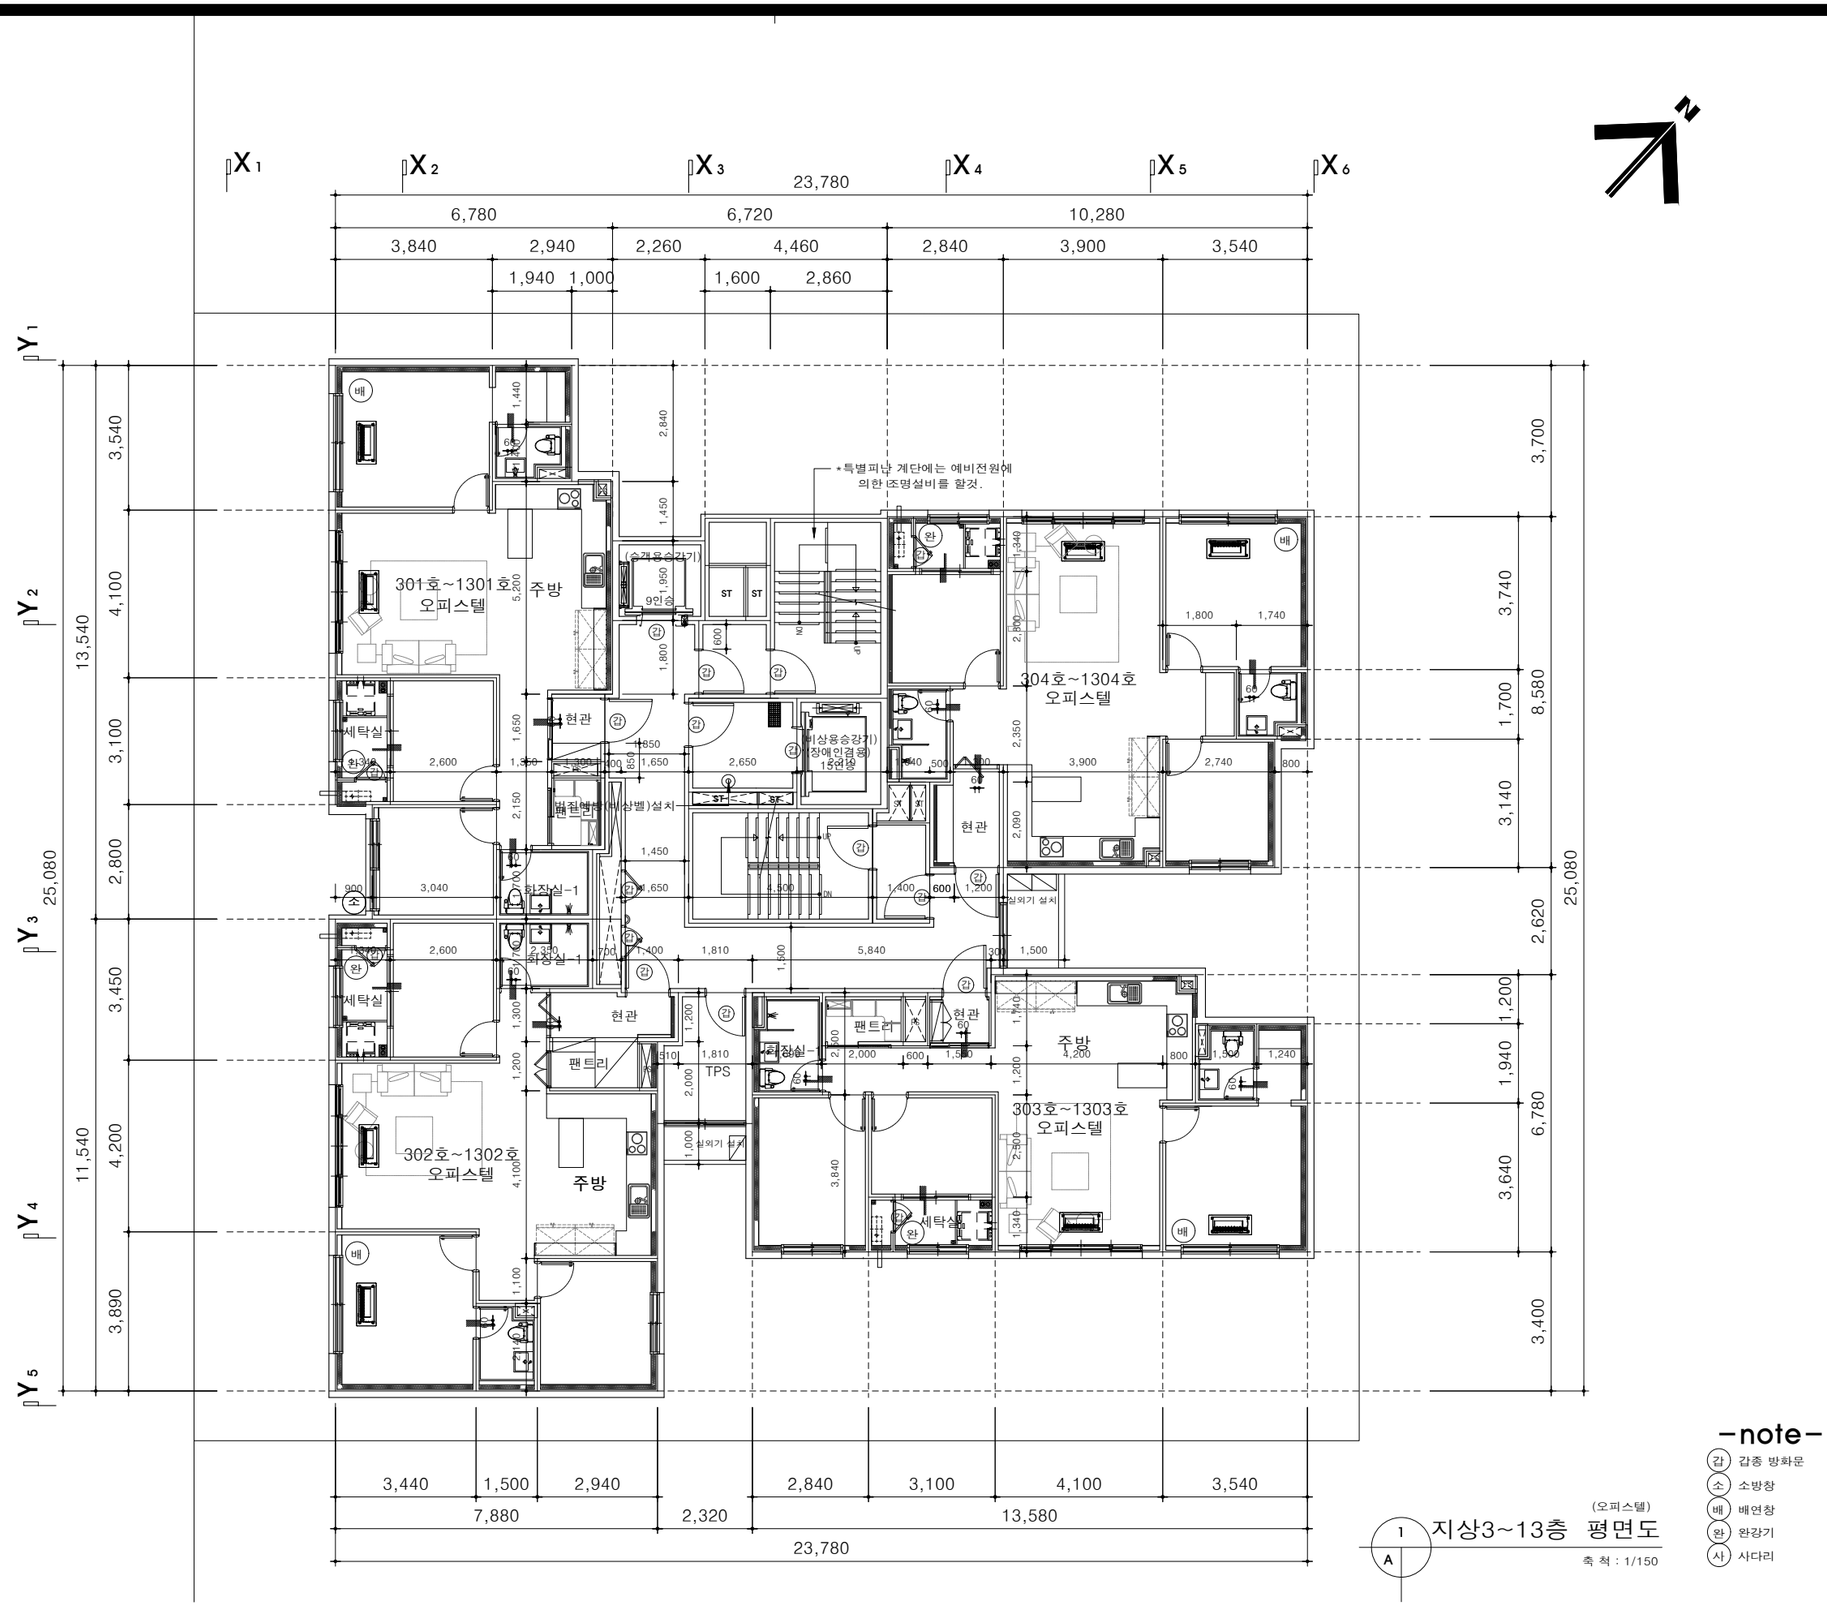

(오피스텔)

지상3~13층 평면도

축 척 : 1/150

-note-

- (갑) 갑종 방화문
- (소) 소방창
- (배) 배연창
- (완) 완강기
- (사) 사다리



(연립주택)


지상14~16층 평면도

축 척 : 1/150

1
A

-note-

- (갑) 갑종 방화문
- (소) 소방창
- (배) 배연창
- (완) 완강기
- (사) 사다리

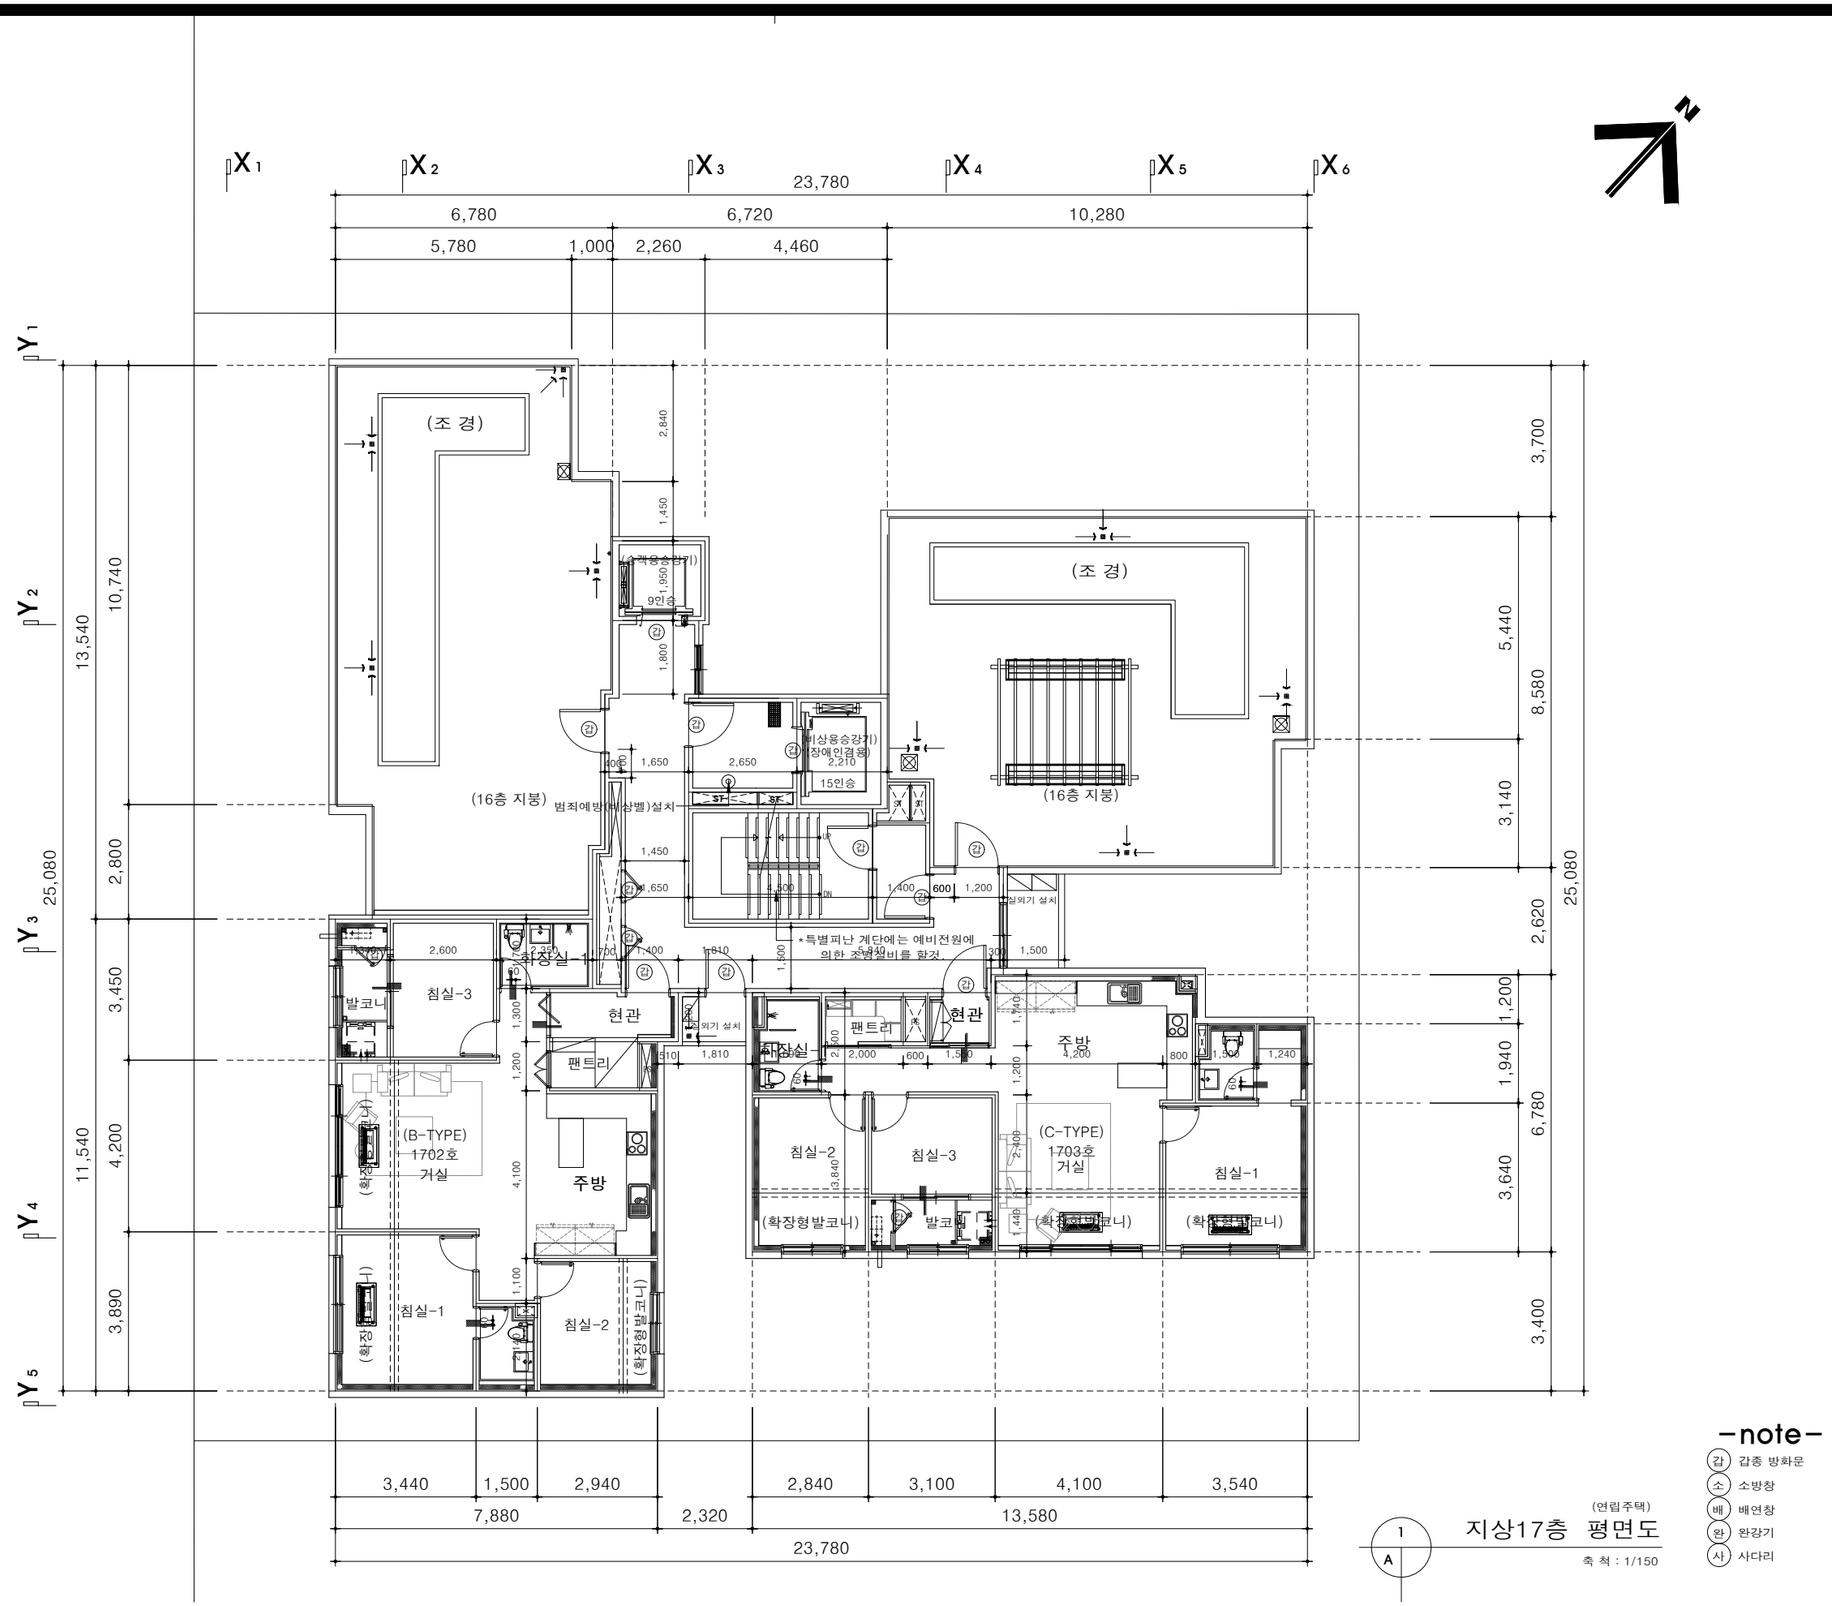

-note-

- (갑) 갑종 방화문
- (소) 소방창
- (배) 배연창
- (완) 완강기
- (사) 사다리

(연립주택)

지상17층 평면도

축 척 : 1/150

1
A